

VERTICAL COMPRESSED-AIR RECEIVER


V-0805 | 4.0 m3 NOMINAL / VERTICAL INSTALLATION

DRAWING: NB-AR-0805-GA-003 REV: A

FICTIONAL PROTOTYPE - NOT FOR FABRICATION


MAIN ARRANGEMENT

EQUIPMENT: V-0805 | 4.0 m3 NOMINAL / VERTICAL INSTALLATION

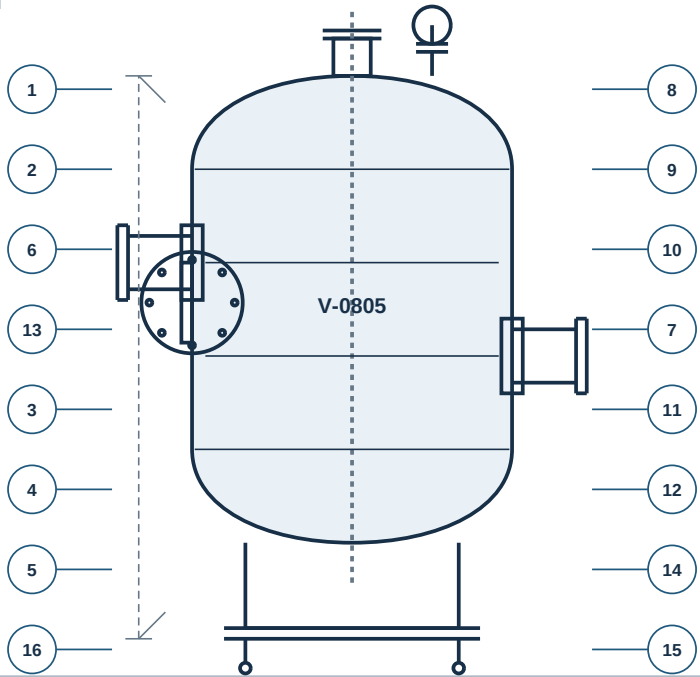

ELEVATION | O/A HEIGHT 3200

DETAIL / CONNECTION VIEW

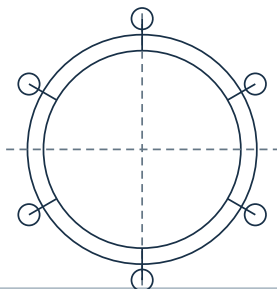

PLAN / NOZZLE ORIENTATION

ITEM	DESCRIPTION	MATERIAL	SIZE	QTY	PART NO
1	VESSEL SHELL COURSE, ROLLED	ASTM A516 GR 70	ID 1500 x 12 THK	1	VS-0805-01
2	TOP TORISPHERICAL HEAD	ASTM A516 GR 70	ID 1500 x 14 THK	1	HD-0805-01
3	BOTTOM TORISPHERICAL HEAD	ASTM A516 GR 70	ID 1500 x 14 THK	1	HD-0805-02
4	SUPPORT SKIRT, CYLINDRICAL	ASTM A36	OD 1512 x 8 THK	1	SK-0805-01
5	BASE RING, ANCHOR BOLT TYPE	ASTM A36	OD 1780 x 25 THK	1	BR-0805-01
6	INLET NOZZLE, REINFORCED	ASTM A105	DN80 / CLASS 150	1	NZ-0805-01
7	OUTLET NOZZLE, REINFORCED	ASTM A105	DN80 / CLASS 150	1	NZ-0805-02
8	SAFETY RELIEF VALVE, SET 10 bar	ASTM A216 WCB	DN25 x DN40	1	PSV-0805-01
9	PRESSURE GAUGE, 0-16 bar	SS 316	DN15 / 100 mm DIAL	1	PI-0805-01
10	PRESSURE TRANSMITTER, 4-20 mA	SS 316	0-16 bar / 1/2 NPT	1	PT-0805-01
11	AUTO DRAIN VALVE, TIMER TYPE	BRASS / SS 304	DN15 / 230 VAC	1	DV-0805-01
12	MANUAL DRAIN VALVE, BALL TYPE	SS 316	DN20 / CLASS 800	1	DV-0805-02
13	MANWAY NECK AND BLIND COVER	ASTM A516 GR 70	DN450 / CLASS 150	1	MW-0805-01
14	MANWAY GASKET, NON-ASBESTOS	ARAMID / NBR	DN450	1	GS-0805-01
15	NAMEPLATE BRACKET, ATTACHED	SS 304	75 x 50 x 6	1	NB-0805-01
16	EARTHING LUG, SHELL	SS 304	50 x 40 x 6	2	EL-0805-01

BILL OF MATERIALS | QUANTITIES ARE PER COMPLETE ASSEMBLY

GENERAL NOTES

- Design pressure 10 bar(g); hydrostatic test pressure to approved vessel code calculations.
- Provide 450 mm clear access in front of manway cover for maintenance.
- All nozzle azimuths are referenced clockwise when viewed from above.

NORTHBRIDGE THERMAL SYSTEMS ENGINEERING PROTOTYPE FICTIONAL EQUIPMENT AND DATA VERTICAL COMPRESSED-AIR RECEIVER	DRAWING NUMBER NB-AR-0805-GA-003	REVISION A	PROTOTYPE SAMPLE NOT FOR FABRICATION Verify all design data
Vessel arrangement, nozzle orientation and fabrication bill of materials	SCALE NTS	SHEET 1 OF 1	before engineering use