


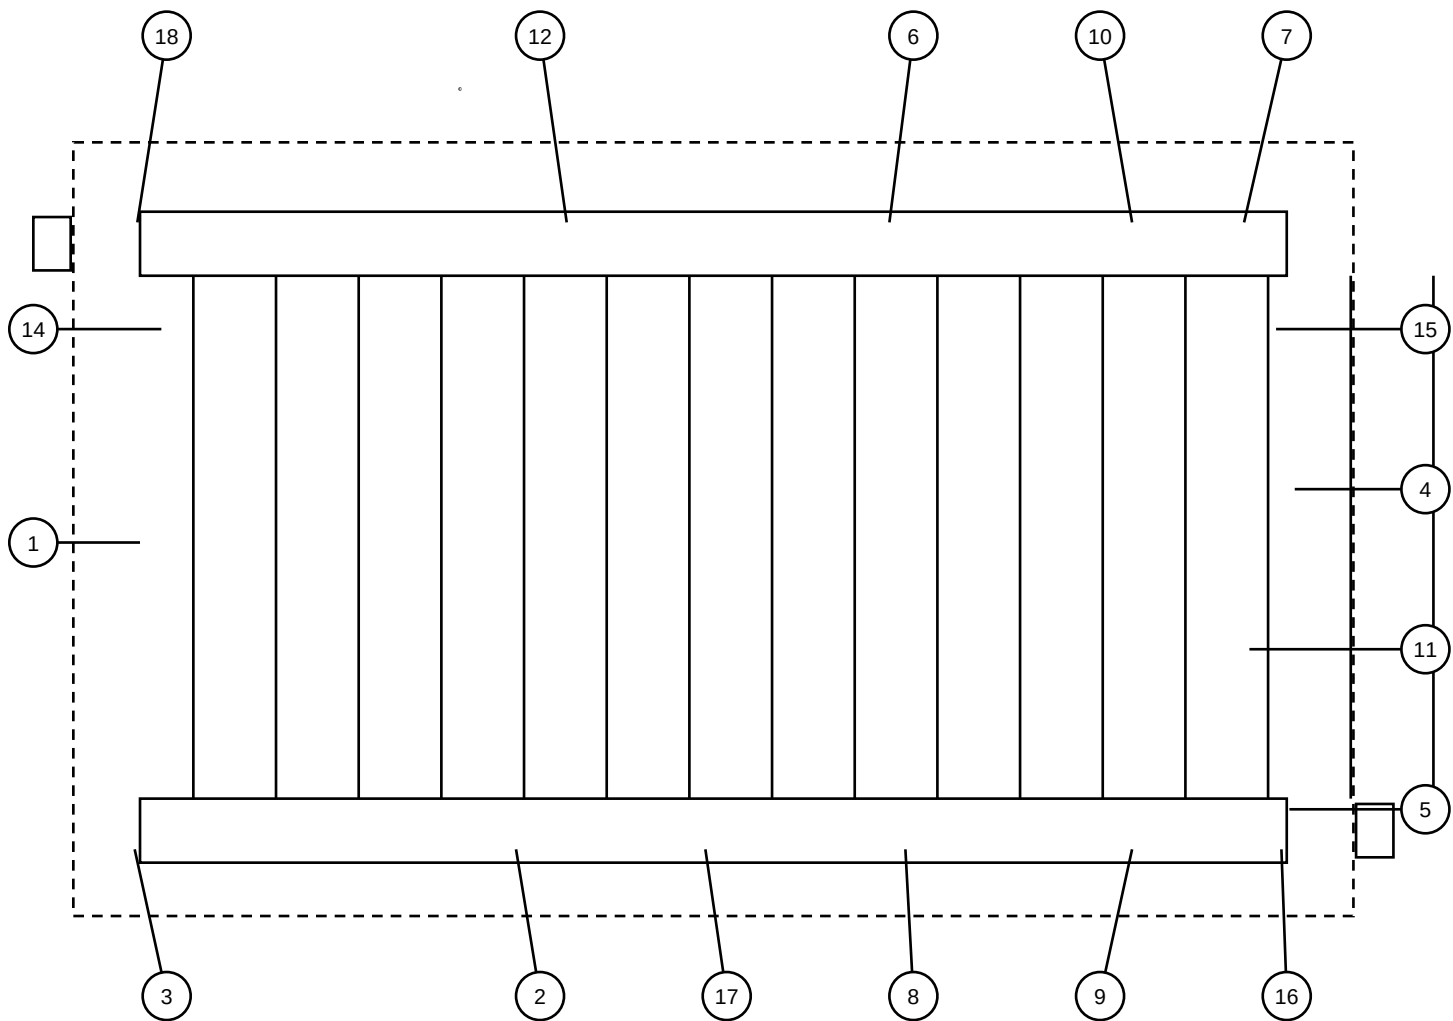

NOTES:

- 1. ALL DIMENSIONS ARE IN MM.
- 2. ALL WELDING AS PER IBR / ASME SEC I.
- 3. INSULATE WITH 100 THK MINERAL WOOL AND CLAD WITH 0.6 THK ALUMINIUM SHEET.
- 4. TUBE QTY IS PER BANK. TYPICAL FOR 4 BANKS.

Pos	Description	Material Spec	Qty
1	INLET HEADER 219.1 OD X 8.0 THK	SA 106 GR.B	1
2	OUTLET HEADER 219.1 OD X 8.0 THK	SA 106 GR.B	1
3	ECONOMISER TUBE 38.1 OD X 3.6 THK	SA 210 GR.A1	108
4	RETURN BEND 38.1 OD	SA 210 GR.A1	40
5	TUBE SUPPORT PLATE 12 THK	IS 2062 GR.B	14
6	INLET FLANGE 200 NB CL.150	SA 105	1
7	OUTLET FLANGE 200 NB CL.150	SA 105	1
8	SAFETY VALVE 50 NB	SA 216 WCB	1
9	DRAIN VALVE 25 NB	SA 105	2
10	VENT VALVE 15 NB	SA 105	1
11	THERMOWELL 1/2 NPT	SS 316	2
12	PRESSURE TAPPING 1/2 NB	SA 105	2
13	STUD BOLT M20 X 90 WITH 2 NUTS	SA 193 B7	16
14	LIFTING LUG 16 THK	IS 2062 GR.B	4
15	CASING PLATE 3 THK	IS 2062	17
16	EXPANSION JOINT 600 X 600	FABRIC	1
17	NAME PLATE	SS 304	1
18	INSPECTION D00R 300 X 300	IS 2062	2

ECONOMISER ASSEMBLY

DRG NO : EC-14-GA-001
DRG REV : B
SCALE : NTS SIZE : A3
SAMPLE (SYNTHETIC) DRAWING